Portfolyo

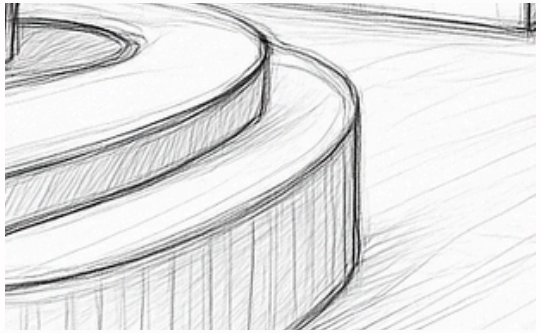

İÇ MİMAR VE ÇEVRE TASARIMCISI / **HİLAL GÖK**

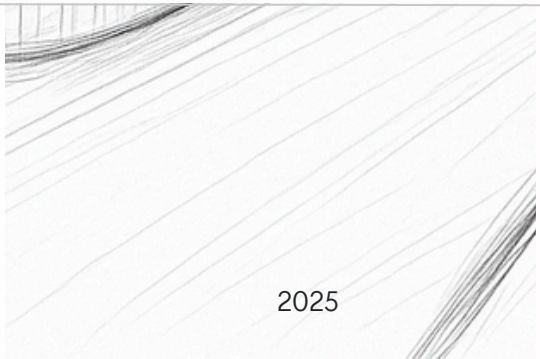

2025

İÇİNDEKİLER

Özgeçmiş

Öğrenci Projeleri

01 Kreş Projesi

02 Mağaza Projesi

03 Huzurevi Projesi

04 Klinik Projesi

05 Peyzaj Toplu Konut Projesi

06 Detay Çizimleri

Serbest Çalışmalar

06 Oturma Odası ve Mutfak Çalışması

07 Banyo Çalışması

Ö Z G E Ç M İ Ş

"Ben Hilal Gök, iç mimarlık yolculuğumda denge, işlevsellik ve estetik arasında bağ kurmayı hedefliyorum. 3D modelleme ve teknik çizim alanında geliştirdiğim becerilerimi, farklı ölçeklerdeki projelere aktarıyorum. Bu portföy, bu süreçte edindiğim deneyimlerden seçilmiş çalışmaları içermektedir."

İLETİŞİM

+90 546 416 23 76

hilalgok094@gmail.com

linkedin.com/in/hilal-gök/

EĞİTİM

2021-2025 Afyon Kocatepe Üniversitesi Güzel Sanatlar Fakültesi İç Mimarlık Ve Çevre Tasarımı Bölümü

2017-2021 Çanakkale İbrahim Bodur Anadolu Lisesi

DENEYİM

ESL Tasarım Mühendislik İnşaat San. ve Tic. Ltd. Şti. - *Şantiye Stajı* 2024

T.C. Çanakkale Belediyesi - *Ofis Stajı* 2023

SERTİFİKA

Memduh Tanrıöver - 3d Studio Max + Corona Eğitim Sertifikası

PROGRAM BİLGİSİ

AutoCAD
3ds Max
SketchUp
Photoshop
Corona
Lumion
Office

DİL BİLGİSİ

İngilizce B1-B2

01-ZEKA KÜPÜ KREŞ

Logo

Bodrum, zemin, birinci kat ve terastan oluşan 642 m2 kapalı, 150m2 açık alanlı kreş projesi.

Zeka Küpü Aktivite Alanı – Galeri boşluğu ile alt-üst mekân ilişkisi güçlendirilmiş, ışık ve renk bloklarıyla canlı bir atmosfer oluşturulmuştur.

Alan, çocukların zihinsel ve bedensel gelişimini destekleyecek şekilde kurgulanmıştır.

Kreşin merkezinde konumlanarak çocukların yaratıcılıklarını geliştirebilecekleri ve sosyal etkileşimlerini artırabilecekleri bir çekirdek mekân işlevi görmektedir.

Programlar: SketchUp + Lumion

Teras, yarı açık mekân anlayışıyla tasarlanmış; gölgelik tavan elemanlarıyla çocuklara güvenli bir oyun ve sosyalleşme alanı sunulmuştur. Alanın çevresi korkuluklarla güvence altına alınırken, farklı yaş gruplarına hitap eden modüler oyun elemanları ve oturma köşeleriyle mekân zenginleştirilmiştir

01-ZEKA KÜPÜ KREŞ

Sınıf mekânında kullanılan sarı tonları, çocuklarda canlılık, neşe ve motivasyonu artırarak öğrenme sürecine pozitif katkı sağlamaktadır. **Uyku o****dasında** tercih edilen yeşil tonları ise sakinleştirici ve huzur verici etkisiyle dinlenme alanında rahatlatıcı bir atmosfer oluşturmaktadır. Renk seçimleri, çocukların duygusal ihtiyaçları ve mekânların işlevlerine göre belirlenmiştir.

0 2 - MAĞAZA PROJESİ

280 m² kapalı alan, AVM içerisinde giyim mağazası işlevine dönüştürülerek planlanmış ve tasarlanmıştır.

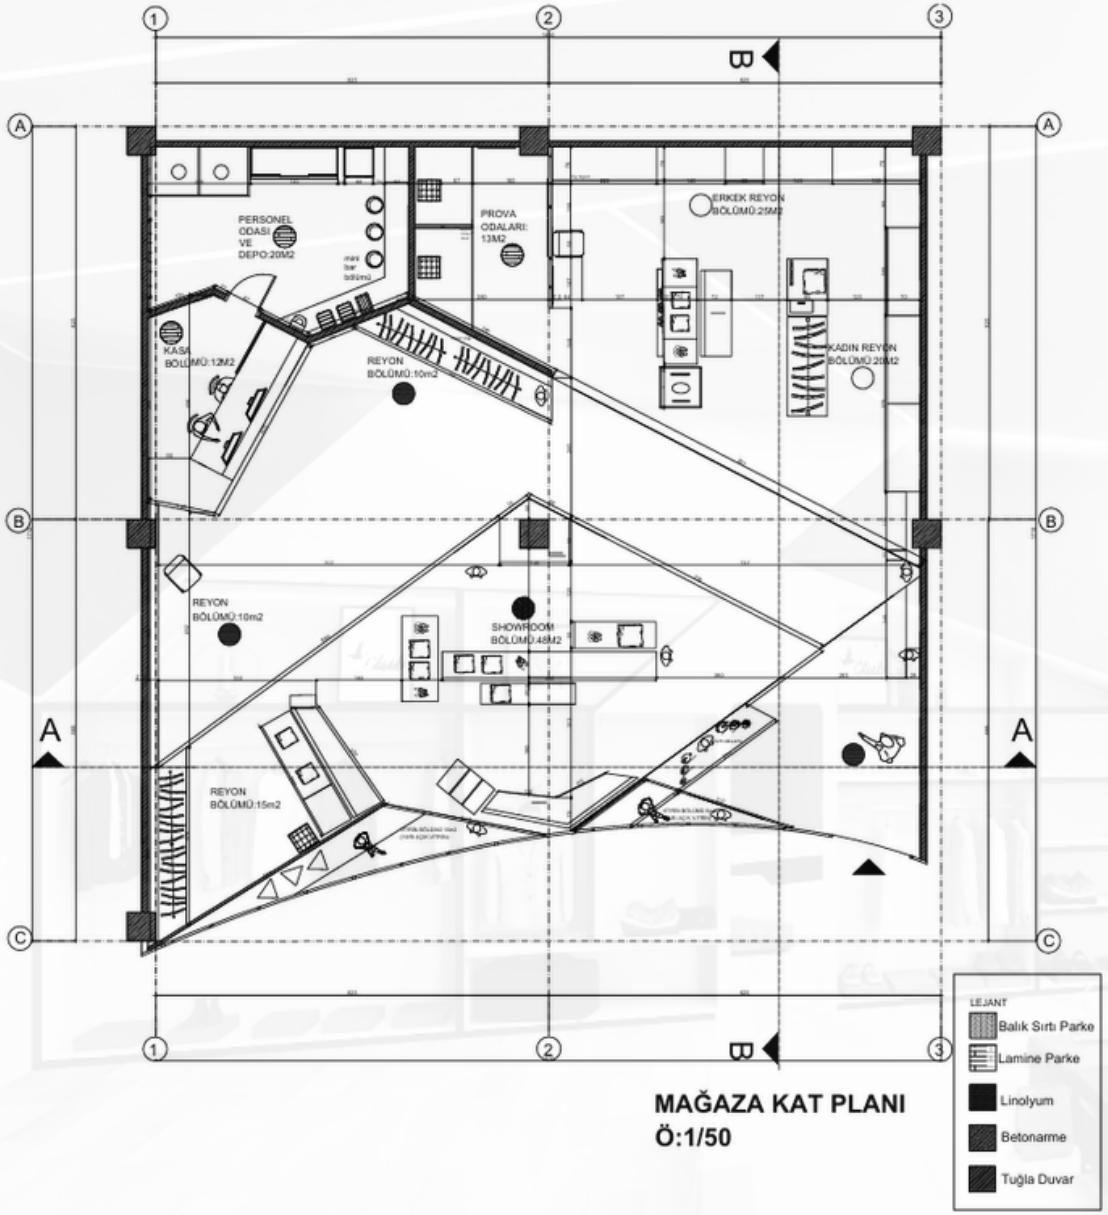

MAĞAZA KAT PLANI
Ö:1/50

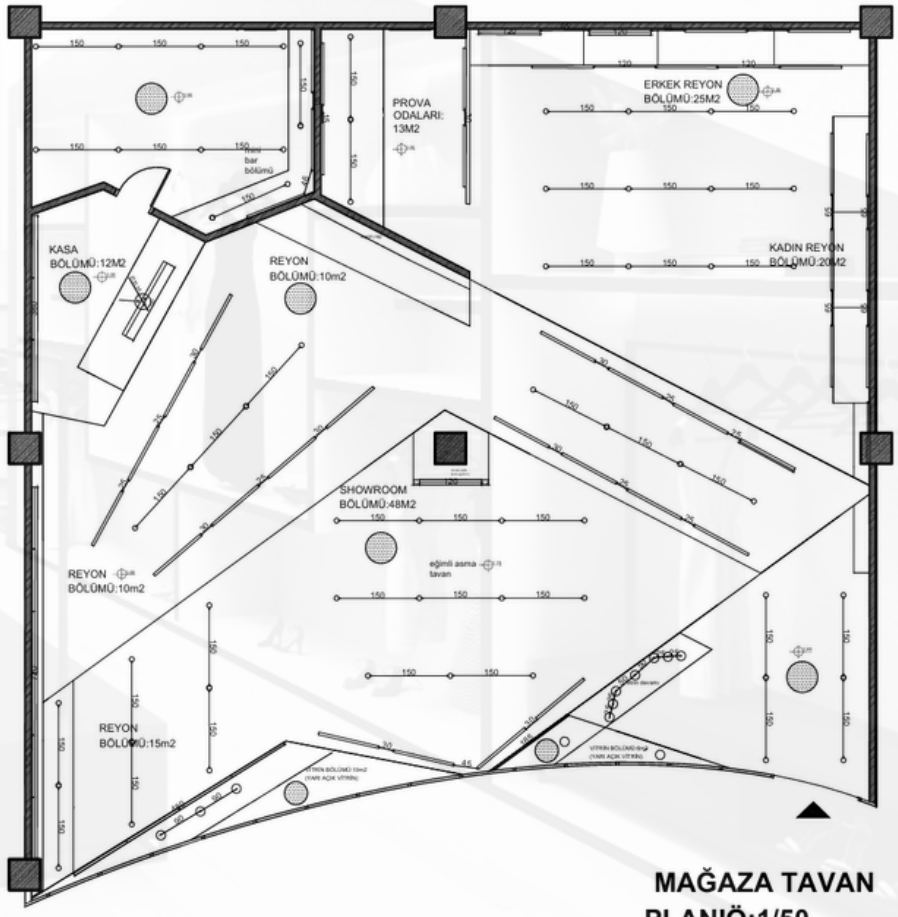

MAĞAZA TAVAN PLANIÖ:1/50

"Asimetrik denge konseptiyle kurgulanan mağaza, dinamik tavan ve duvar geometrileriyle mekâna hareket katmıştır. Doğal ahşap zemin ve modern aydınlatma elemanları, çağdaş ve davetkâr bir alışveriş atmosferi oluşturur."

02 - MAĞAZA PROJESİ

Vitrin bölümü, markanın lüks anlayışını yansıtan modern bir tasarımla ele alınmış; asimetrik formlar ve aydınlatma detayları, markanın vizyonuna uygun prestijli bir sergileme alanı oluşturmuştur

02 - MAĞAZA PROJESİ

Programlar: SketchUp + Lumion

02 - MAĞAZA PROJESİ

Farklı ölçeklerdeki formlar ve hacimler, ziyaretçiye hareketli bir mekânsal deneyim sunarken ürünlerle etkileşimi güçlendirmektedir. Asimetrik denge anlayışıyla kurgulanan sergileme üniteleri ve dolaşım alanları, mekânda yönlendirici bir akış yaratmakta; kullanıcıya modern ve dinamik bir alışveriş atmosferi sağlamaktadır.

02 - MAĞAZA PROJESİ

Kasa bölümü, müşterinin alışveriş deneyimini konforlu şekilde tamamlaması için sade ve fonksiyonel bir yaklaşımla tasarlanmıştır. Dolaşım sistemi, mağaza içinde yönlendirmeyi kolaylaştıracak şekilde kurgulanmış, akışın doğal ve kesintisiz olması sağlanmıştır.

02 - MAĞAZA PROJESİ

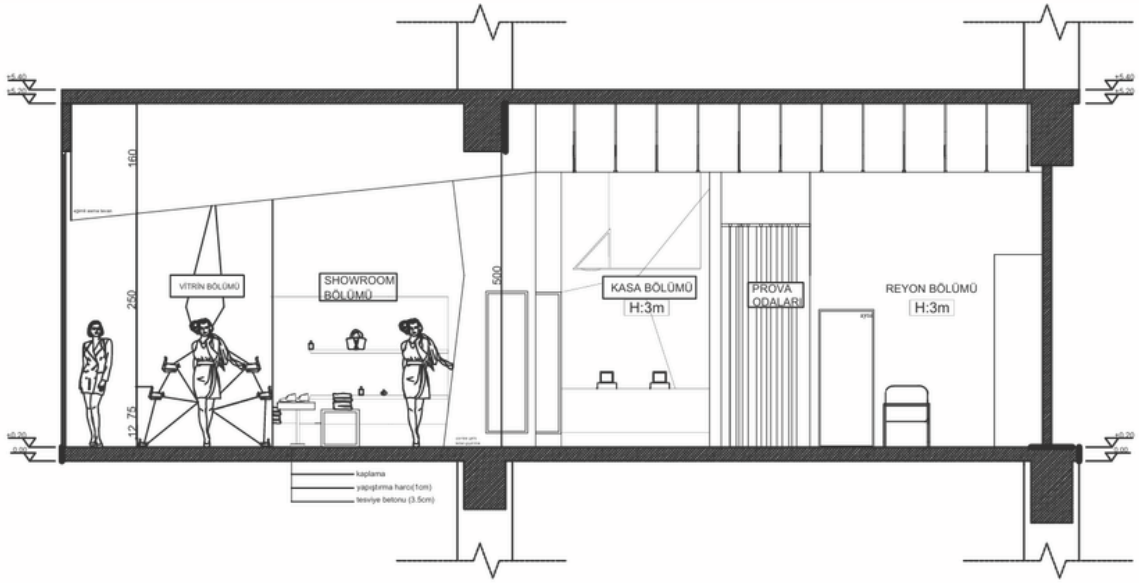

B-B KESİTİ Ö:1/50

0 3 - HUZUREVİ PROJESİ

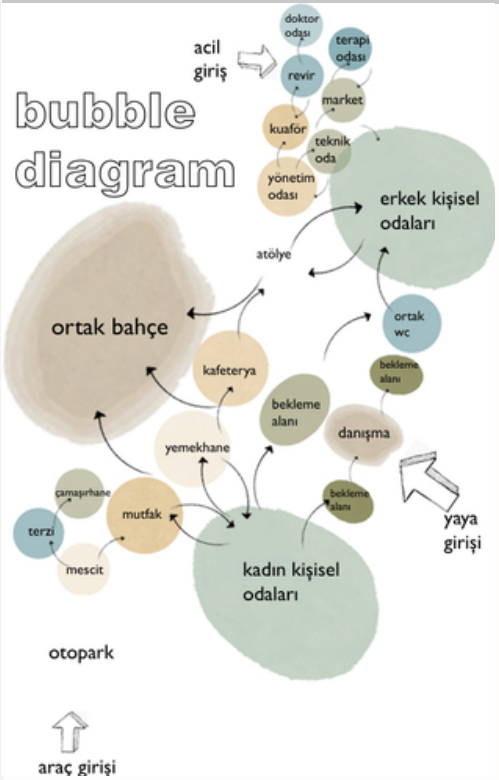

1200 m2 kapalı alana sahip tek kat huzurevi yarı açık ve açık alanlarıyla huzurlu bir ortam olarak tasarlanmıştır.

ÖZEL
Zeytin Dalı
HUZUREVİ

Huzurevi tasarımında, doğanın büyüme sürecinden esinlenen eksensel koram hiyerarşisi mekâna yansıtılmıştır. Ahşap dokular, doğal taş ve yeşil tonlarıyla desteklenen malzeme seçimi, merkezden çevreye doğru gelişen mekânsal akışa doğallık ve süreklilik kazandırmıştır

Programlar: SketchUp + Lumion+Autocad

Danışma Render Çalışma

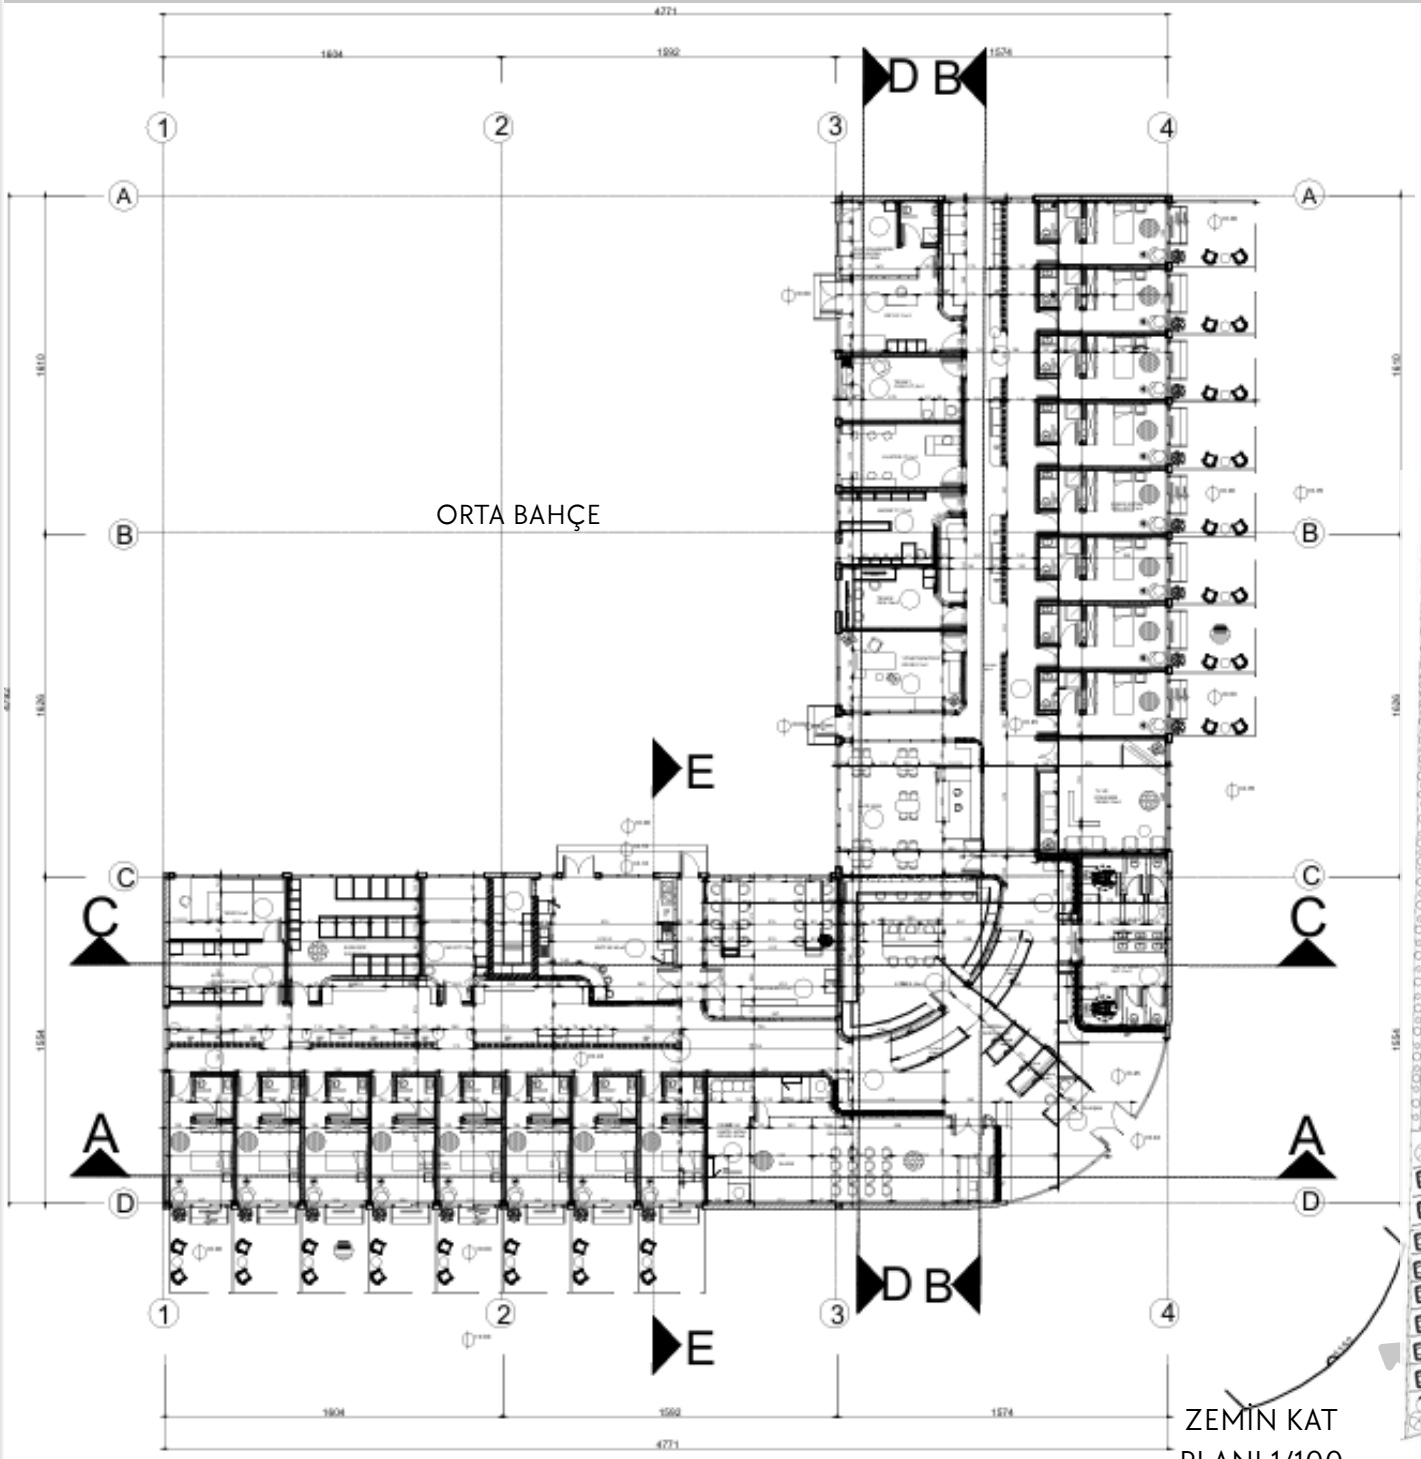

ZEMİN KAT
PLANI 1/100

VAZİYET
PLANI 1/500

03-HUZUREVİ PROJESİ

Danışma Render Çalışması

03-HUZUREVİ PROJESİ

Atölye Render Çalışması

Atölye girişinde mekâna davetkâr bir etki katmak için lineer ahşap ve dairesel formda asma tavan uygulamaları kullanılmıştır. Bu farklı tavan türleri hem giriş aksını vurgulamış hem de iç mekâna ritmik bir hareket kazandırmıştır.

03-HUZUREVİ PROJESİ

Atölye Render Çalışması

Organik formlar ve doğal malzemelerle bütünleşen bu tasarım, sakin ve huzurlu bir çalışma deneyimi sunmak üzere kurgulanmıştır.

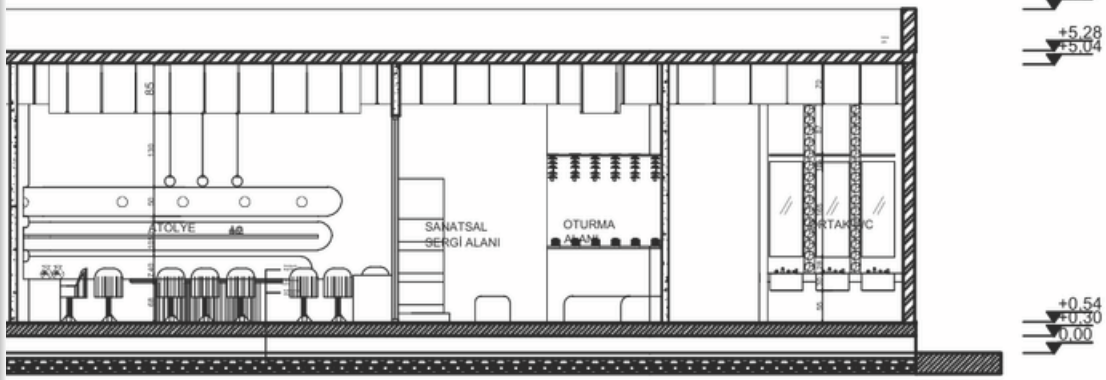

B-B KESİTİ

800 m² kapalı alana sahip, iki katlı klinik projesi; modern tasarım dili, fonksiyonel planlama ve kullanıcı odaklı mekân kurgusuyla tasarlanmıştır.

0 4 - KLİNİK PROJESİ

Giriş Render Çalışması

Programlar: 3dsmax+ Corona+Phhotoshop+Autocad

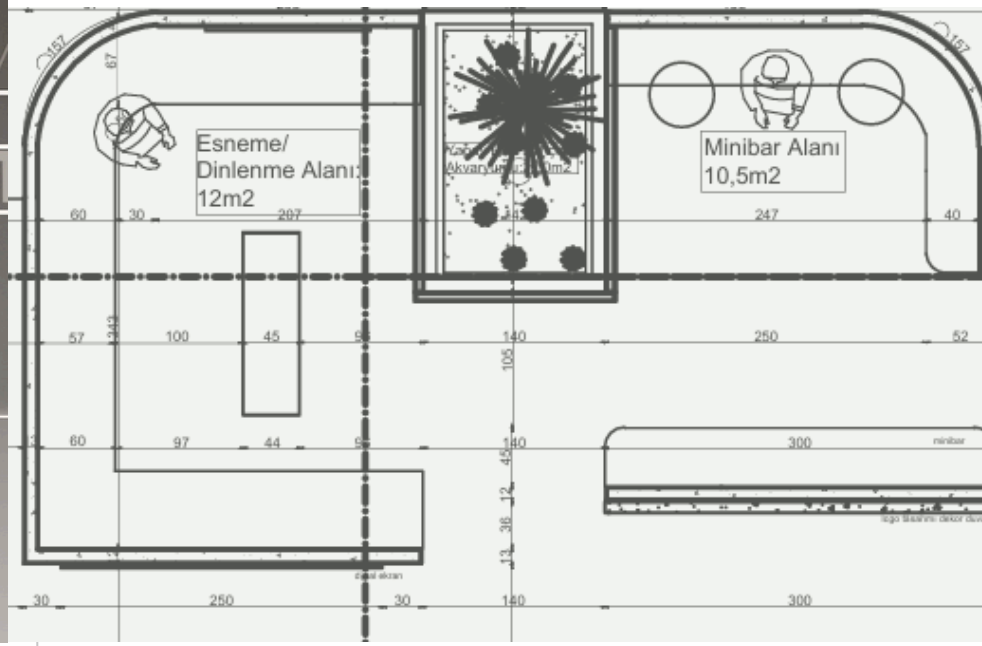

Danışma Render Çalışması

04 - KLİNİK PROJESİ

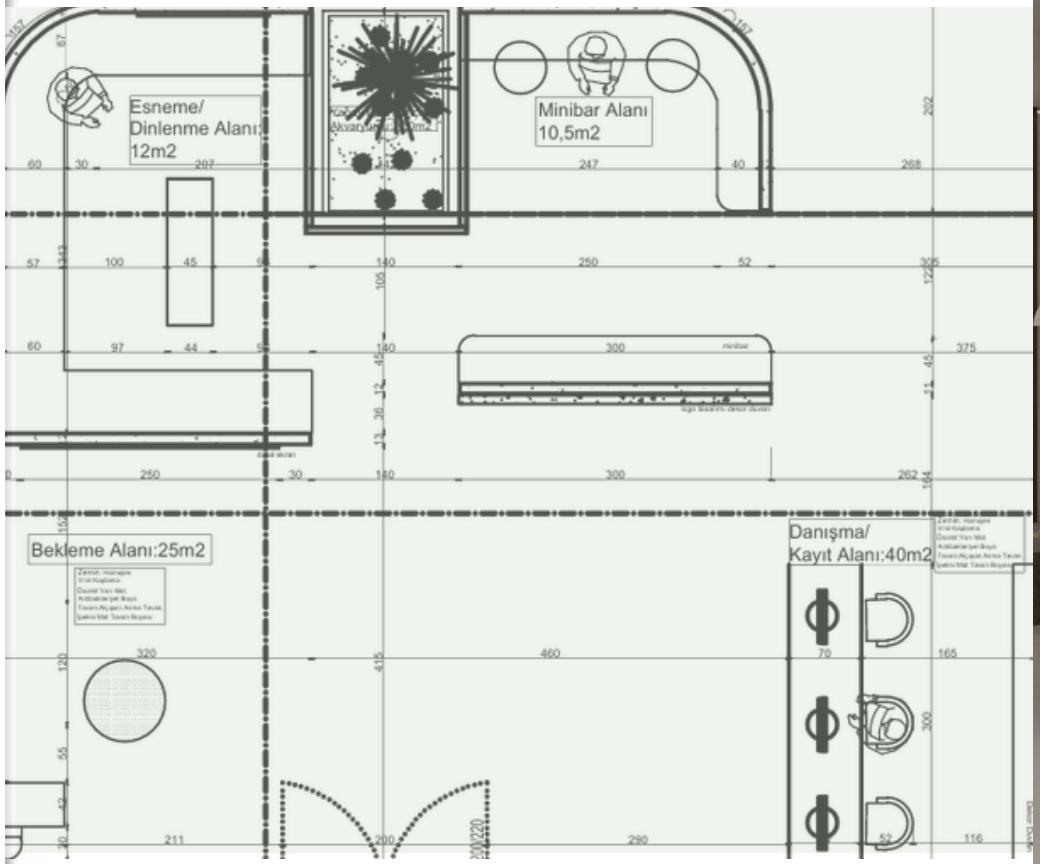

Danışma Render Çalışması

04 - KLİNİK PROJESİ

Muayene Odası Render Çalışması

Minimal ve fonksiyonel bir yaklaşım benimsenmiştir. Açık renk paleti, doğal ışığı maksimum düzeyde içeri alarak ferah ve hijyenik bir atmosfer yaratmıştır. Lineer aydınlatmalar, sade mobilya seçimleri ve yalın geometriler mekânın çağdaş ve güven verici mimari dilini pekiştirmiştir.

Bekleme AlanıRender Çalışması

04 - KLİNİK PROJESİ

Egzersiz Odası
Render Çalışmaları

0 5 - PEYZAJ PROJESİ

Grup Çalışması: Hilal GÖK & Semra USLU

Programlar: SketchUp + Lumion

Projenin animasyonunu izlemek için okutun.

Afyon'daki toplu konut yerleşkesi için hazırlanan bu peyzaj projesinde, kullanıcıların sosyalleşebileceği açık alanlar, yaya odaklı ulaşım aksları ve dinlenme bölgeleri tasarlanmıştır. Bölgeye özgü bitki türleri kullanılarak doğal çevreyle uyum yakalanmış, aynı zamanda sürdürülebilir bir yeşil doku oluşturulmuştur.

TOPLU KONUT BİTKİSEL TASARIM PEYZAJ PROJESİ

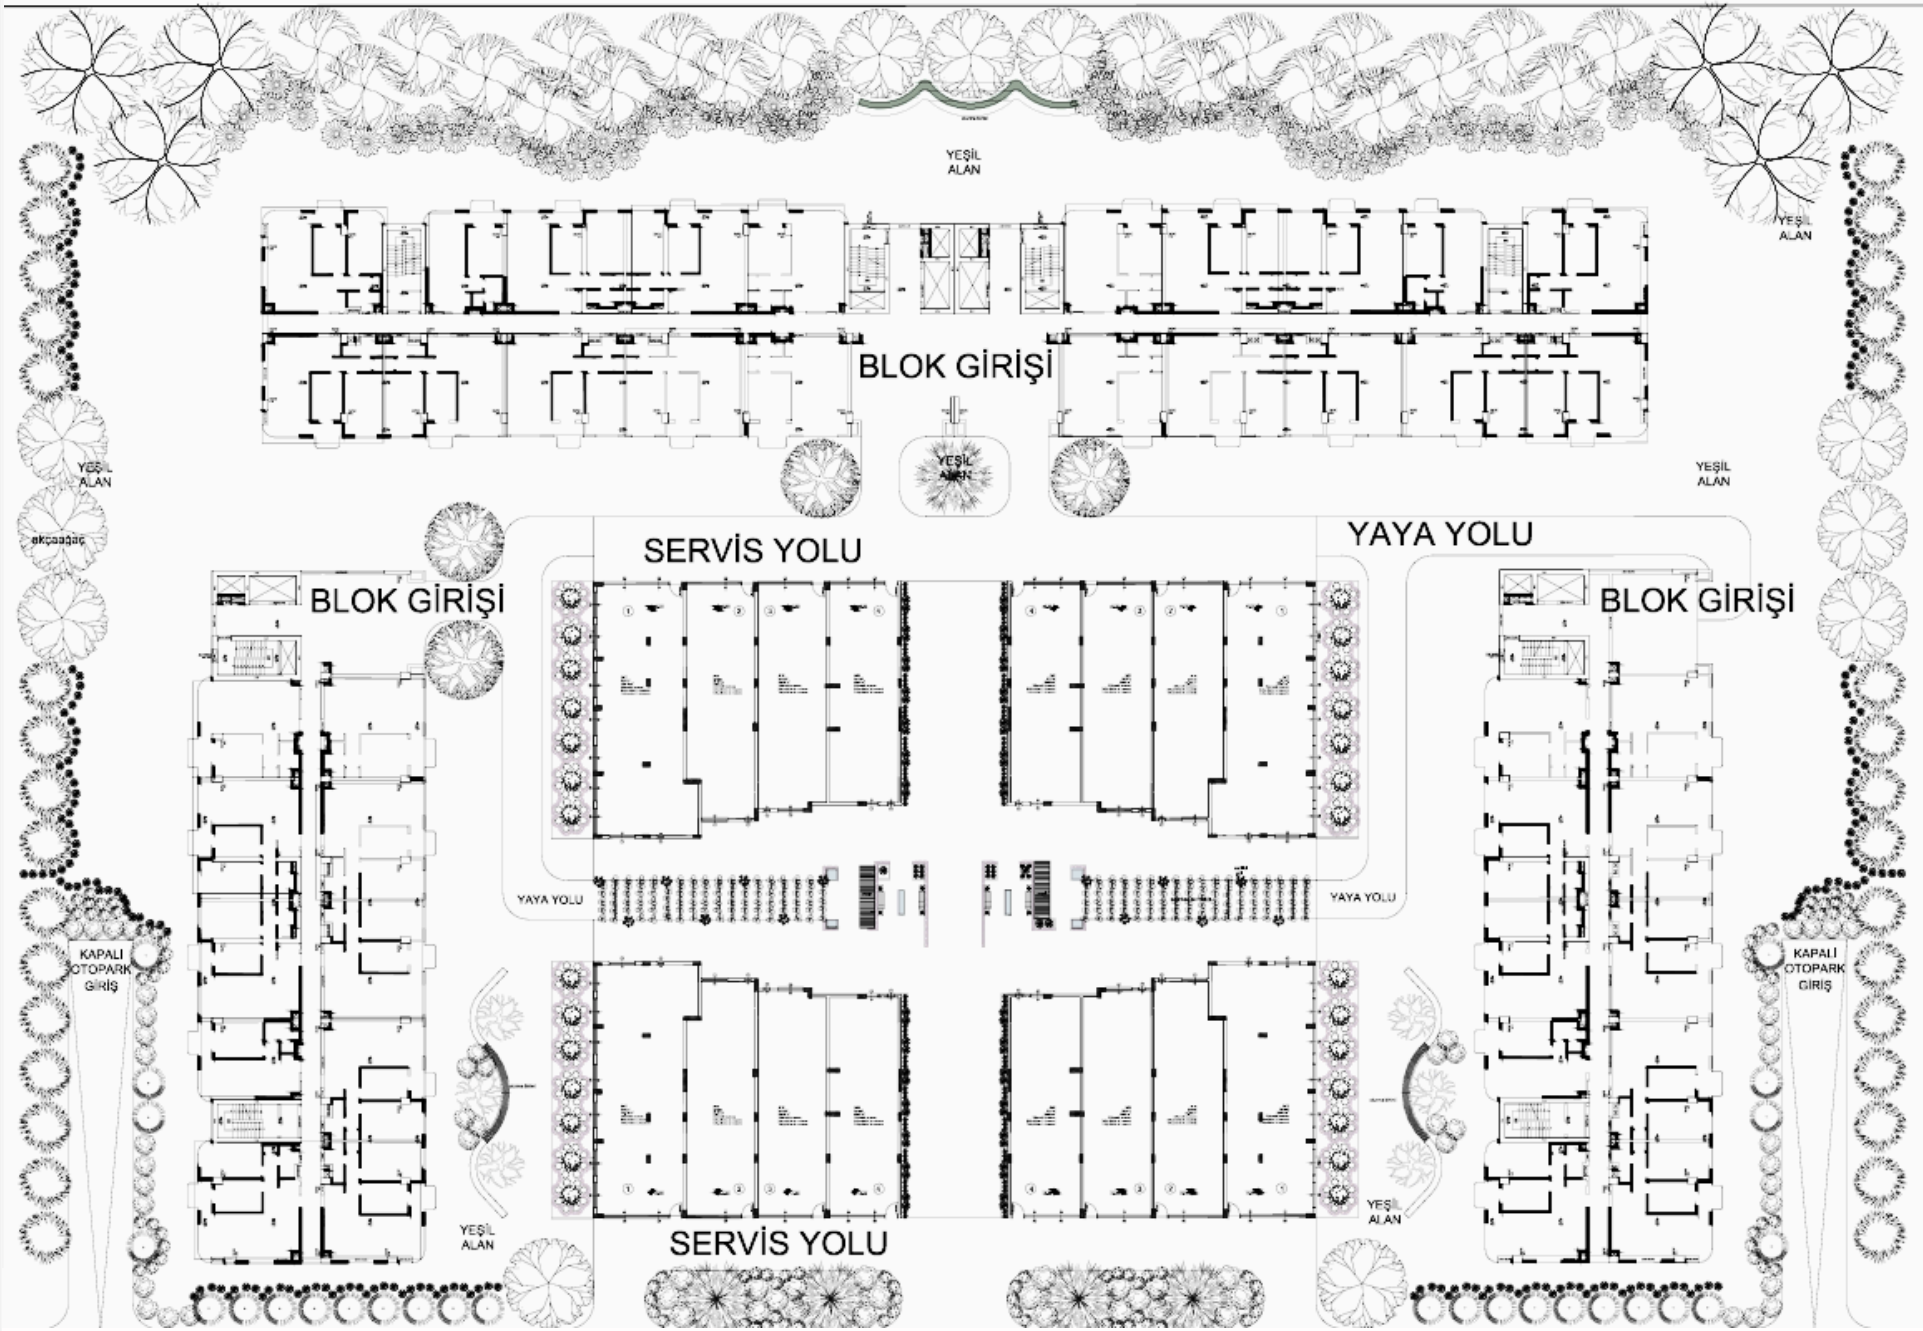

İBRELİ AĞAÇLAR

NO	KODU	SEMBOL	LATİNCE ADI	TÜRKÇE ADI	ADET
1	Pi Ni		Pinus nigra subsp. nigra	Karaçam	5
2	Cu Se		Cupressus Sempervirens	Servicağı Ağacı	10

GENİŞ YAPRAKLI AĞAÇLAR

NO	KODU	SEMBOL	LATİNCE ADI	TÜRKÇE ADI	ADET
3	Ac Ne		Acer negundo	Akçaağaç	11
4	Ce Si		Celtis silvestris	Çitlembik	20
5	Ul Ca		Ulmus campestris	Dağ Karaağacı	6
6	Di Ki		Diospyros kaki	Hurma	4
7	Pl Or		Platanus orientalis	Doğu Çınarı	20
8	Ti Ta		Tilia Tomentosa	Ihlamur	6

ÇALILAR

NO	KODU	SEMBOL	LATİNCE ADI	TÜRKÇE ADI	ADET
9	Be Th		Berberis thunbergii	Berberis	154
10	Bu Se		Buxus sempervirens	Şimşir	80
11	Ey Ja		Euonymus japonicus	Japon	173
12	Ho Ti		Hebe x franciscana 'Blue Gem'	Hebe	88
13	Ru Ha		Rosa hemisphaerica Sweet	Sarı Gülüşah	90
14	Ru Ni		Lonicera Nitida	Lonicera	167

TIRMANICI VE SARILICILAR

NO	KODU	SEMBOL	LATİNCE ADI	TÜRKÇE ADI	ADET
15	Pa Qu		Parthenocissus quinquefolia	Amerikan Sarmaşığı	154
16	Ro Al		Rosa alberica var. macrantha	Sarılıcı Gül	10

AFYON KOCATEPE ÜNİVERSİTESİ
GÜZEL SANATLAR FAKÜLTESİ
İÇ MİMARLIK VE ÇEVRE TASARIMI BÖLÜMÜ

PROJE DÖNEMİ	:	2024-2025 BAHAR DÖNEMİ
TESLİM TARİHİ	:	30.05.2025
PROJE YÜRÜTÜCÜSÜ	:	HİLAL GÖK 21305600
ÖĞRENCİ NUMARASI	:	SEMRA USLU 21305604
PROJE İÇERİĞİ	:	PLAN PAFTASI
ÖLÇEK	:	1/10
PROJE KONUSU	:	TOPLU KONUT BİTKİSEL TASARIM PROJESİ
DERSİN ADI VE KODU	:	BİTKİSEL TASARIM / SD 422
DERSİN YÜRÜTÜCÜSÜ	:	DR. ÖĞR. ÜYESİ EMRAH MUTLU

NOT: İdarenin isteğine bağlı olarak bitki sayıları %5 ile %10 arası artırılabilir.

05 - PEYZAJ PROJESİ

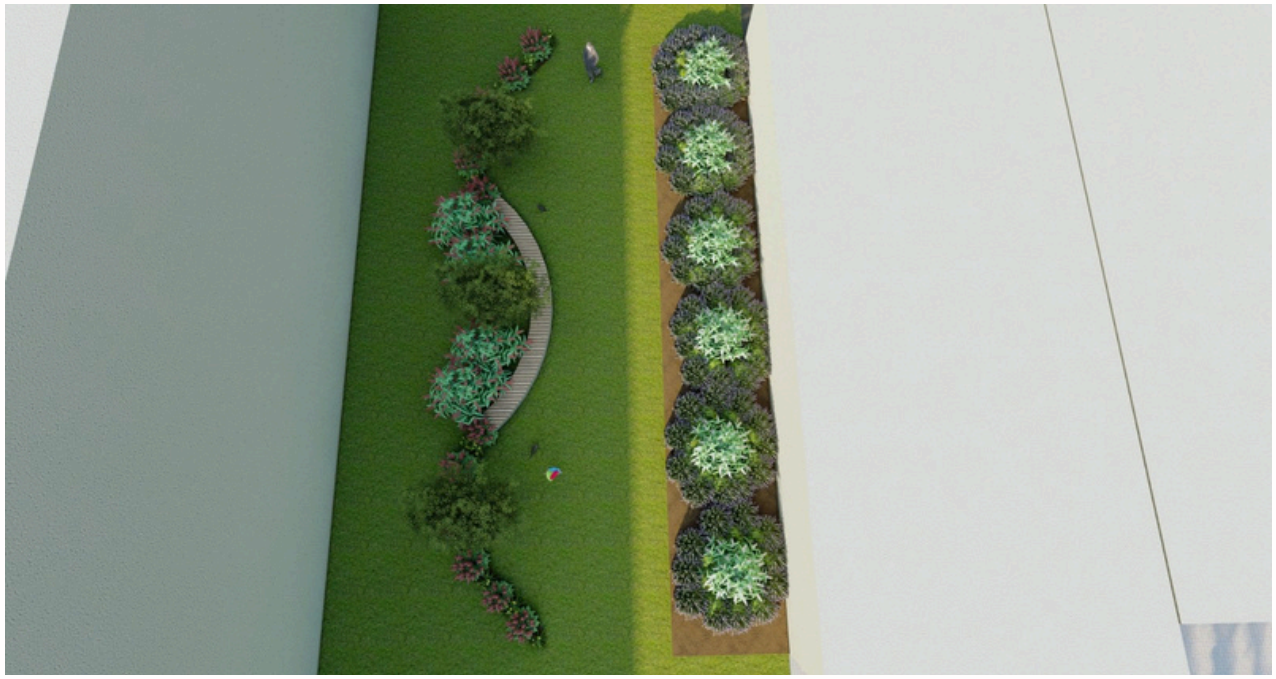

05 - PEYZAJ PROJESİ

05 - PEYZAJ PROJESİ

DETAY MOBİLYA ÇİZİM DETAYLARI

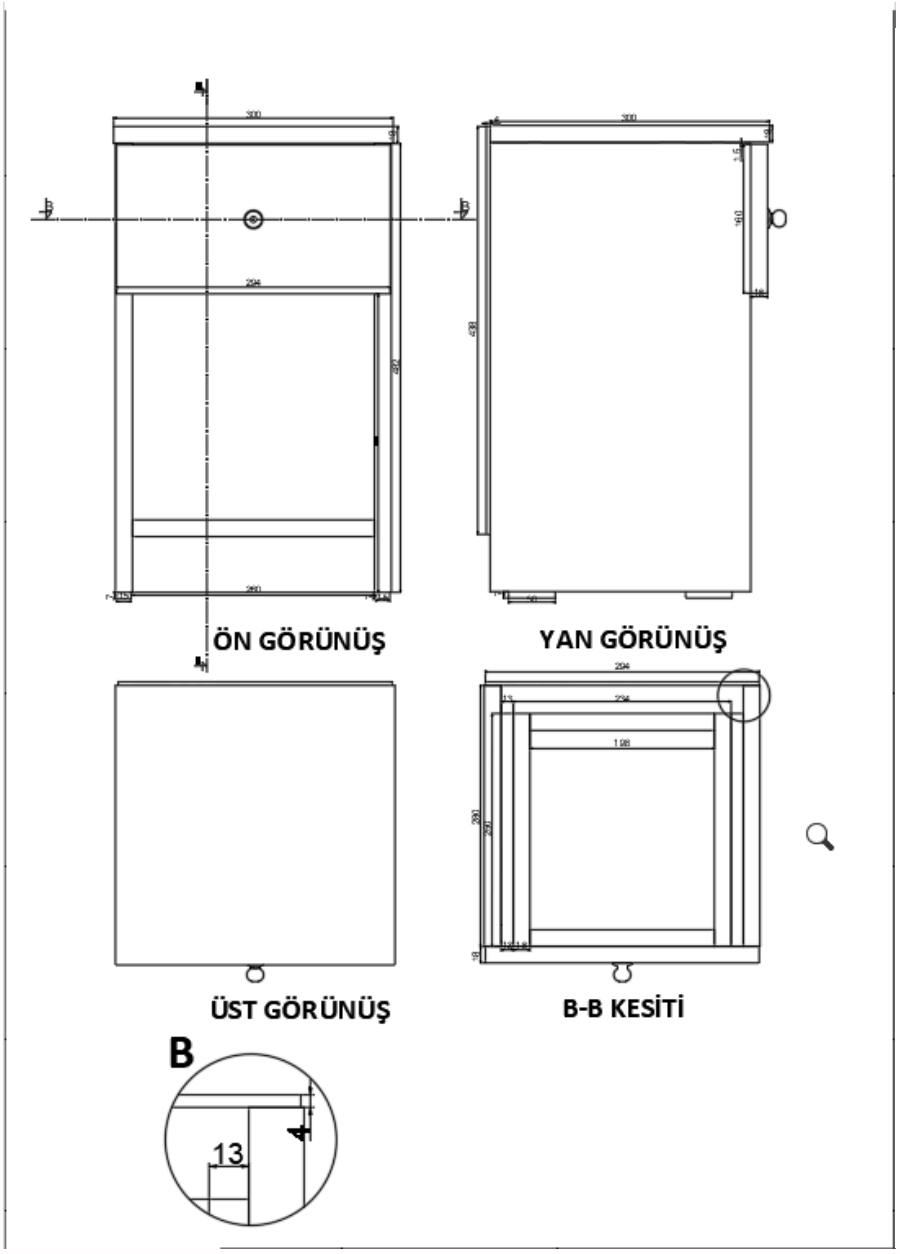

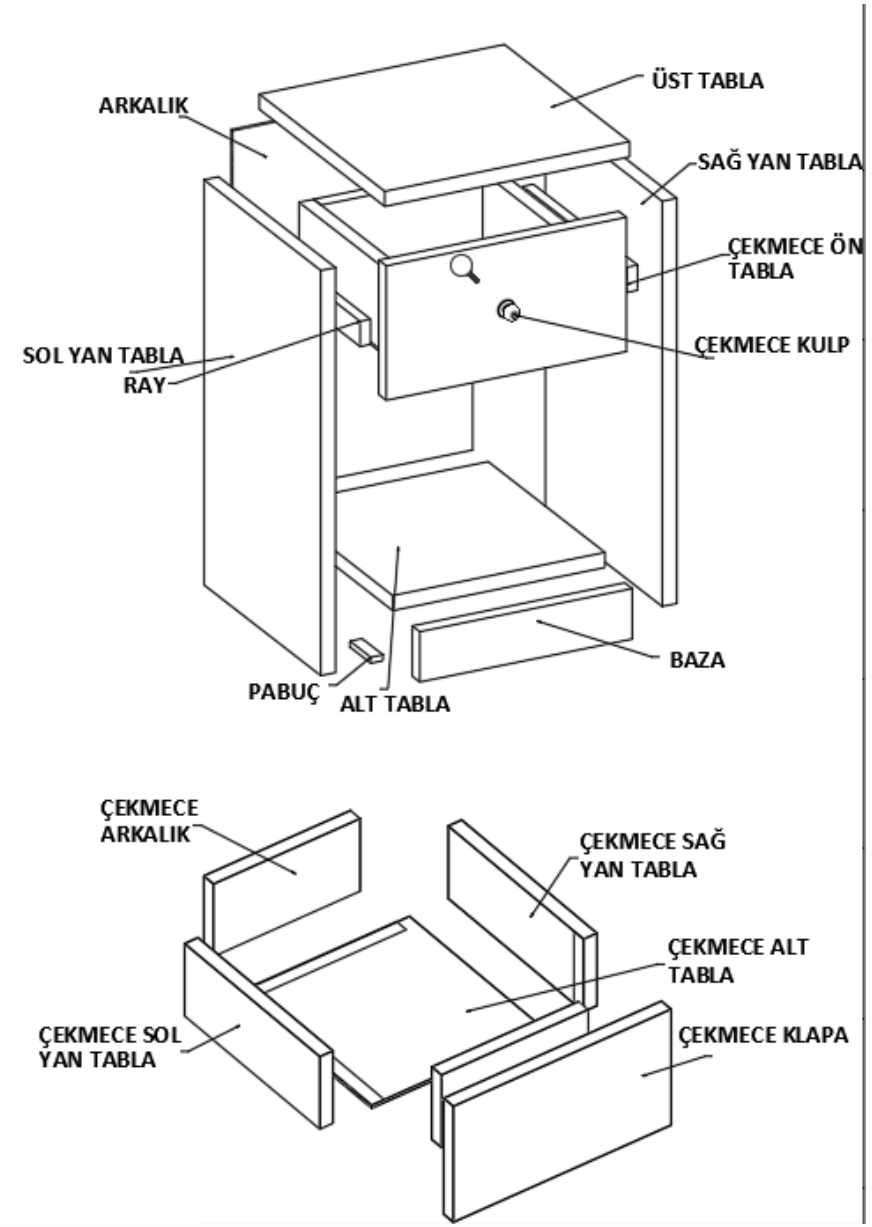

Süs Havuzu Detay Çizimi DETAY NO : 1

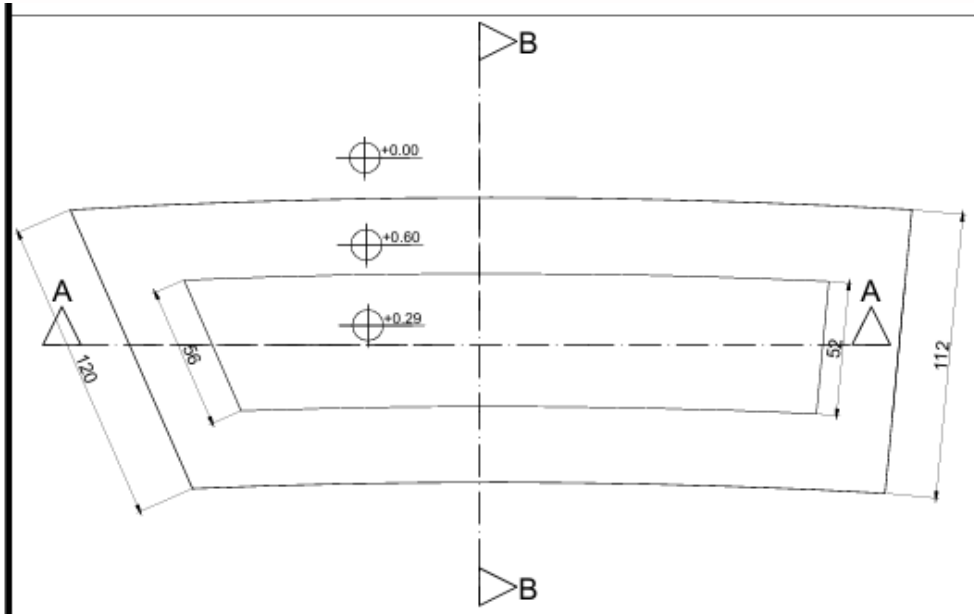

PLAN GÖRÜNÜŞÜ Ö:1/20

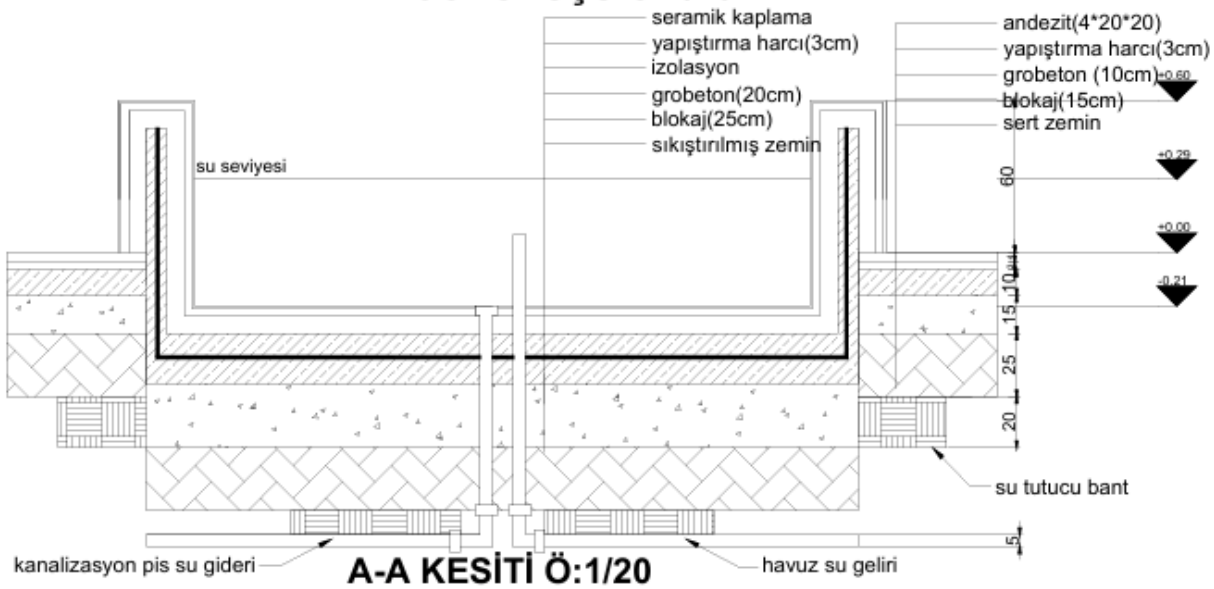

A-A KESİTİ Ö:1/20

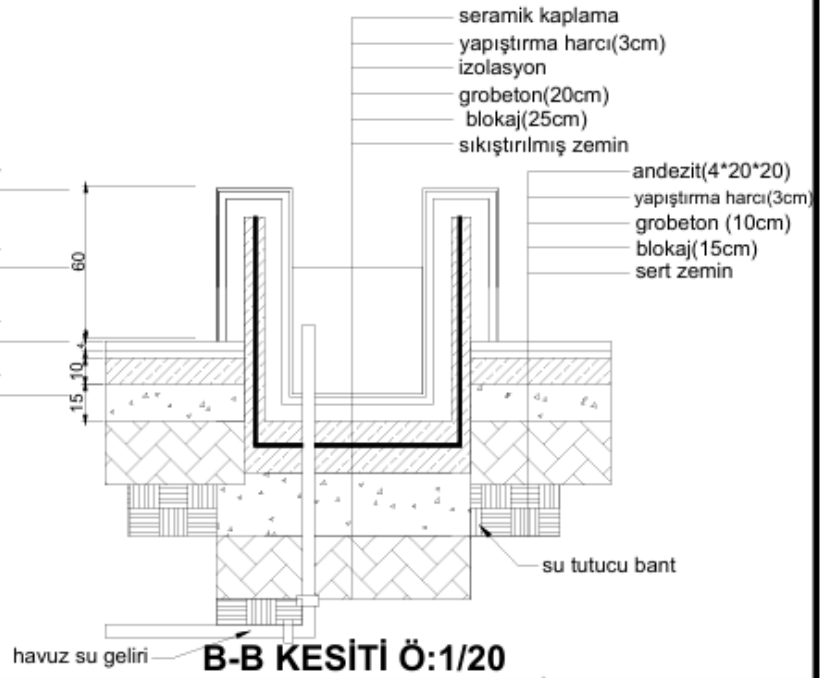

B-B KESİTİ Ö:1/20

OTURMA ODASI ÇALIŞMALARI

0 6 -SERBEST ÇALIŞMALAR

Endüstriyel dokuların modern çizgilerle buluşup, doğal ışığın mekânla kurduğu ilişki öne çıkarılmıştır

2025

SCHIELE

Beton dokular, doğal ışık ve sade mobilya seçimleriyle endüstriyel bir atmosfer kurgulanan bu mekânda; modern çizgilerle dengelenmiş sıcak detaylar öne çıkar. Doğal bitkiler ve aydınlatma öğeleri mekâna yaşam enerjisi katar.

MUTFAK ÇALIŞMASI

BANYO ÇALIŞMALARI

Soft tonlarla ve doğal aksesuarlarla spa etkisi veren bir banyo tasarlanmıştır.

Minimal detaylar ve sıcak aydınlatmalar mekâna rahatlatıcı bir kimlik kazandırır.

T E Ş E K K Ü R L E R

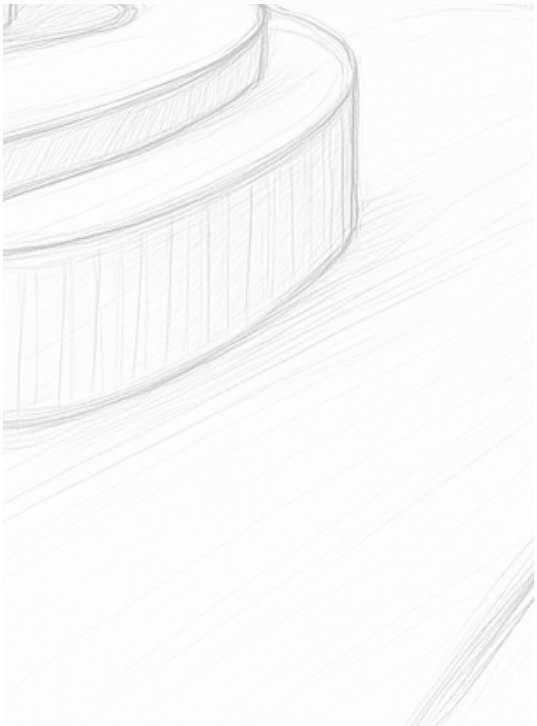

Dijital portfolyo için tarayınız.